


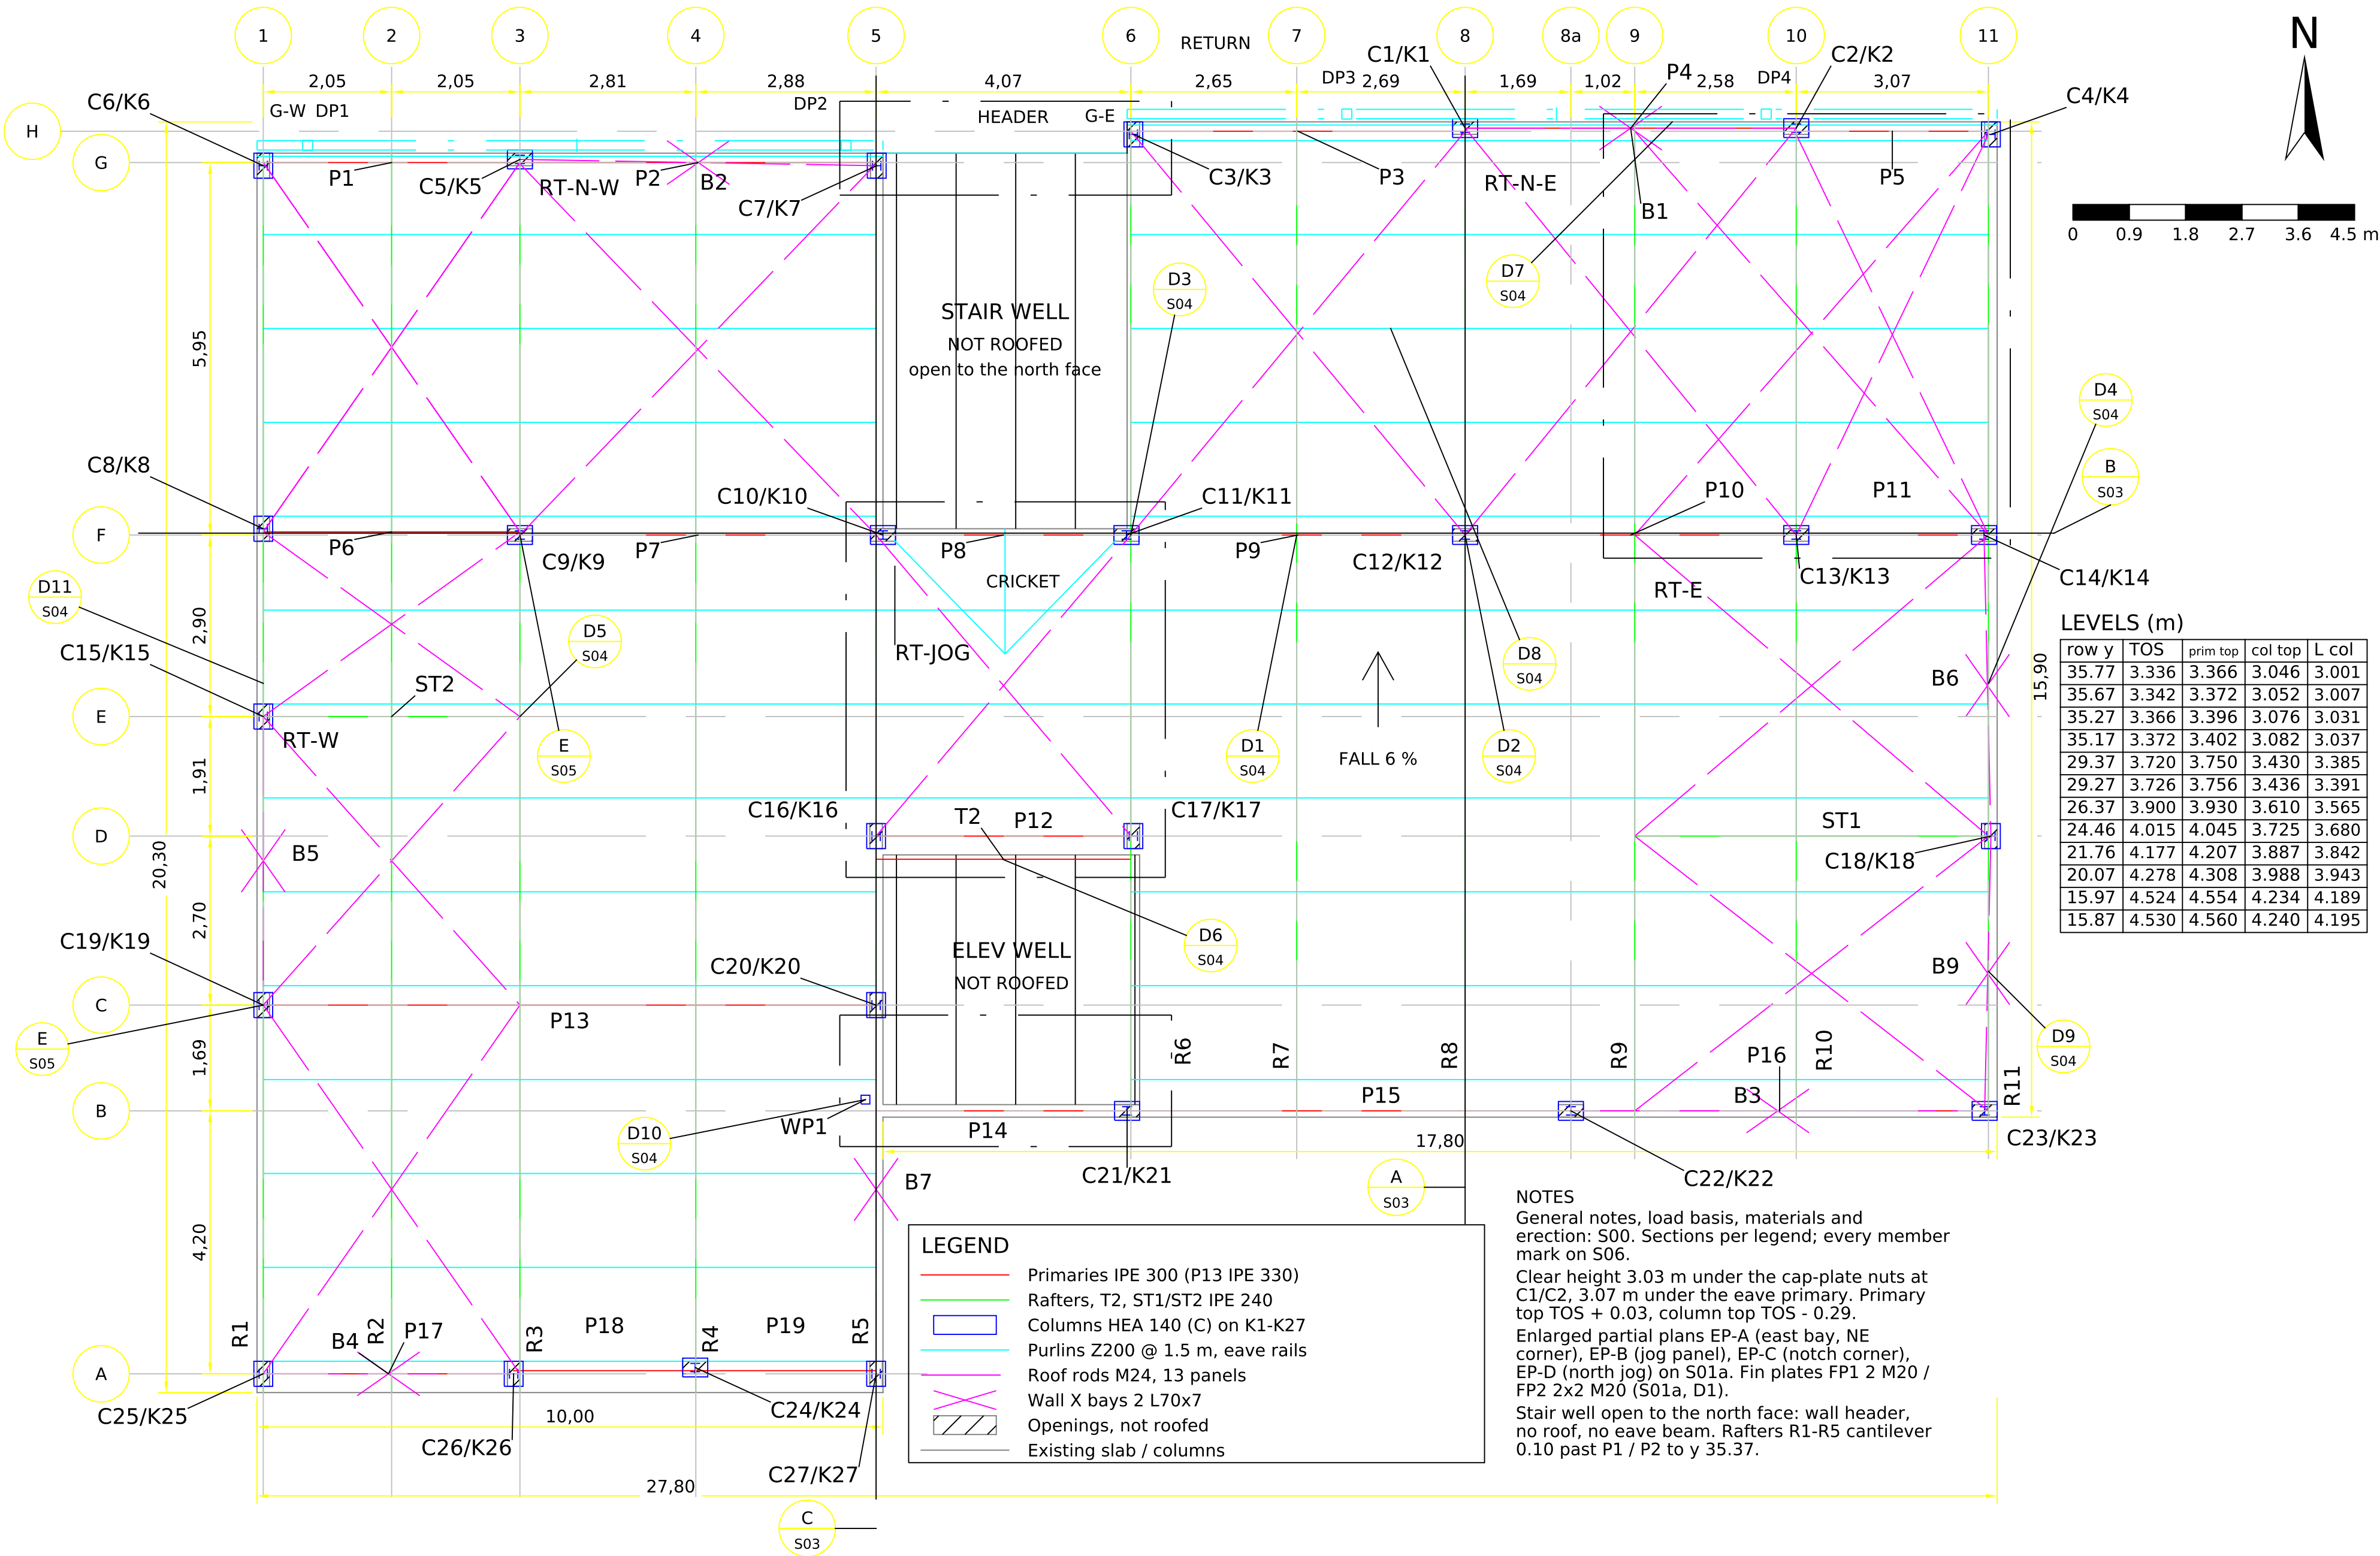

PROJECT

Steel roof - Administration Building, Regatta Tourist Village, Tripoli

ALTERNATIVE C - POST-AND-BEAM BRACED STEEL ROOF, SANDWICH PANELS

Client: Regatta Tourist Village, Tripoli Issued by: Eng. MALEK ABOZRAIG (malek.abozraig@gmail.com) Units: m

SHEET TITLE

ROOF FRAMING PLAN

Scale 1:1 in model space (m); print 1:200 on A1

Status: ISSUED FOR CONSTRUCTION subject to the site verification of S00 section 9

REVISIONS			
3	2026-09-29	Rev 6a (IPE 300/240, HEA 140), bases Rev 8, bracing Rev 5a	
2	2026-09-28	Design Rev 3 / bases Rev 4b (critique C1-C15)	
1	2026-09-27	First issue: design Rev 2, bases Rev 3	

CURRENT REVISION

Rev 6a superstructure
Rev 8 bases / bracing Rev 5a

DATE 2026-09-29

Drawn: Designed:
Checked: Approved:

DRAWING No.
RTV-ST-S01

S01