


SECTION NOTES
A-A: north on the right; rafter R8 9.20 m span; C1 and C12 in section; gutter G-E at the north eave. Clear height 3.03 m under the cap-plate nuts at C1/C2, 3.07 m under the eave primary P4.
B-B: east on the right; rafters R1-R11 beyond shown dashed; stair well beyond open to the north face. C-C: north on the right; R5 ends at y 35.37 (west north edge); bay B7 C27-C20; WP1 beyond.


SECTION A-A rafter line 8 (x 87.19), looking west

RAFTER R8 IPE 240: 9.20 m span, fin plates FP1 (D1), fly braces at the third points (D8)
P15 IPE 300

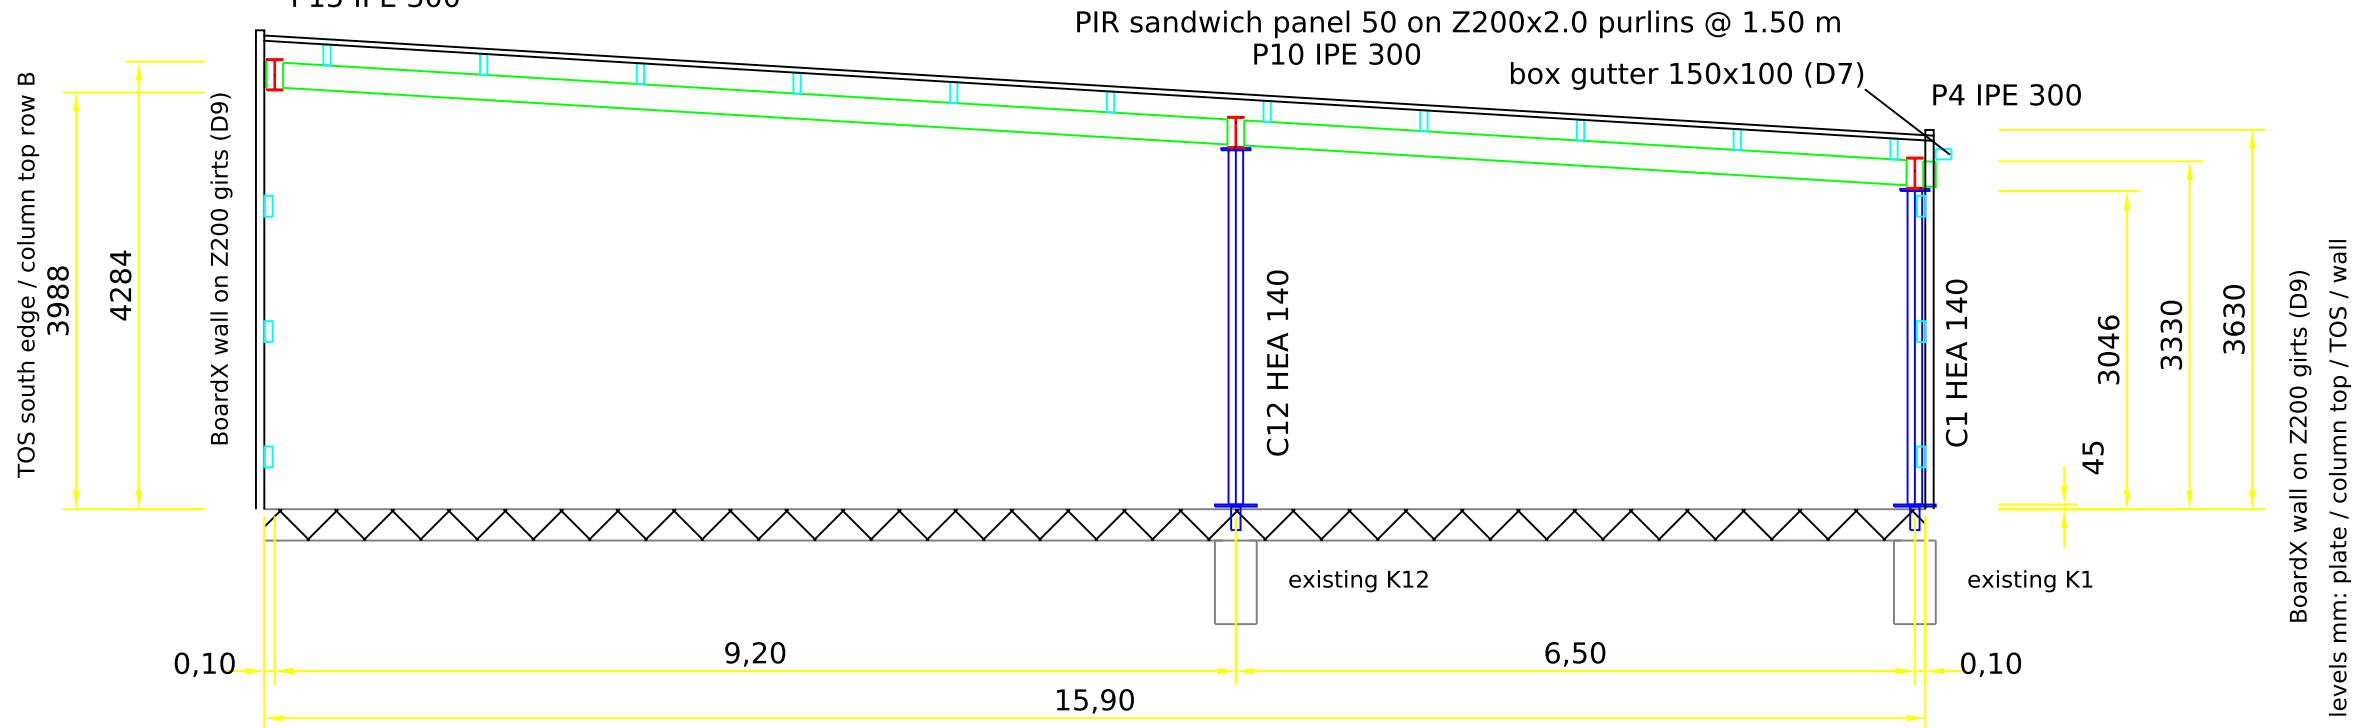


SECTION B-B primary row F (y 29.27), looking north

STAIR WELL beyond (open to the north face): 150 upstand on P8 / R5 / R6 (D6), cricket north of P8
P7 IPE 300 P9 IPE 300

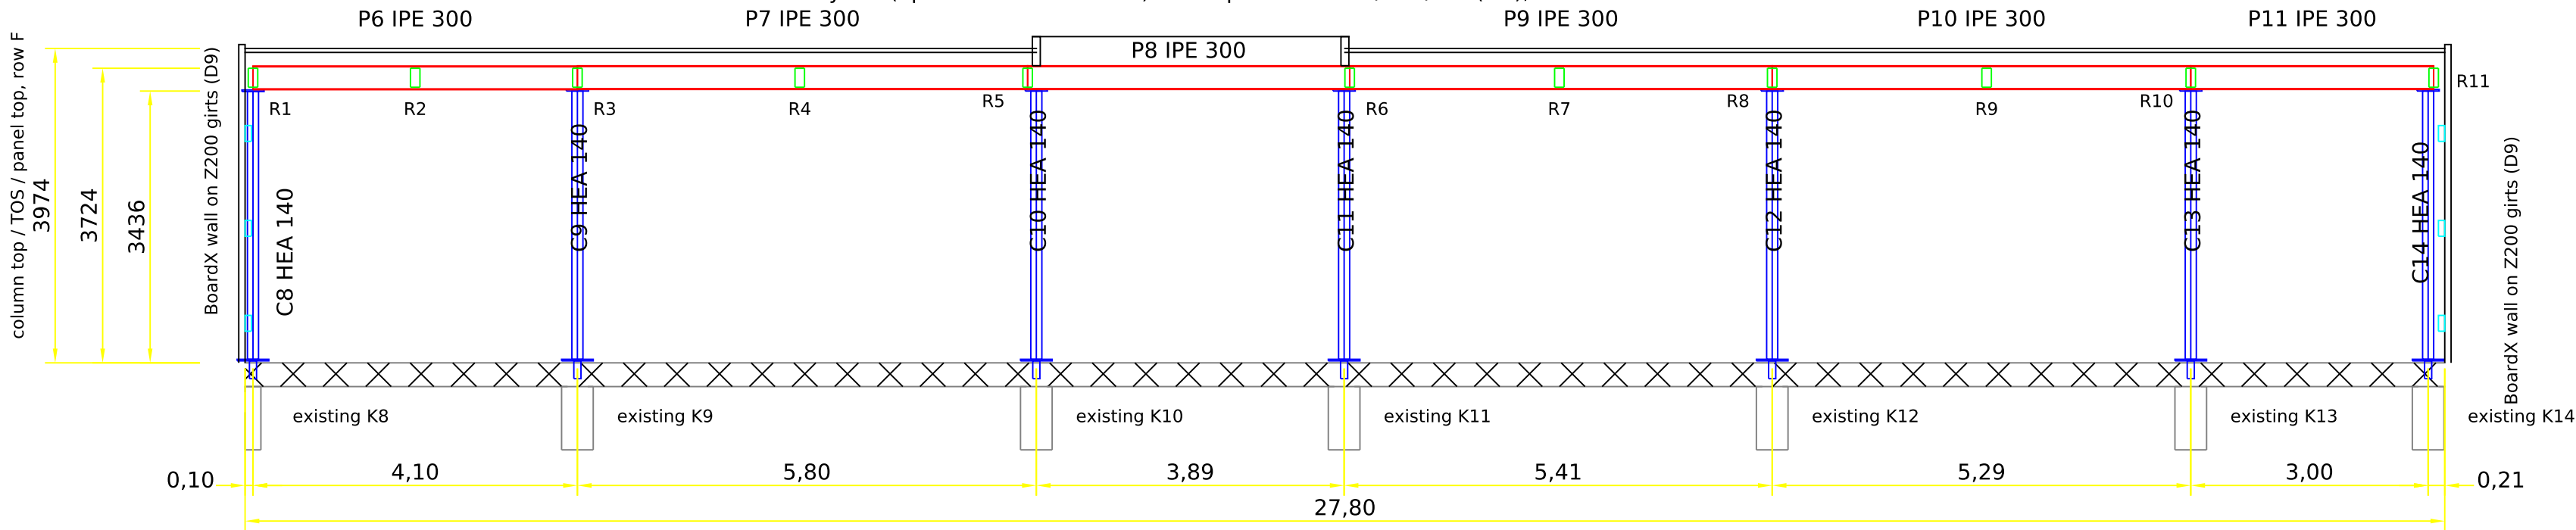

SECTION C-C braced line 5 (x 77.78), looking west

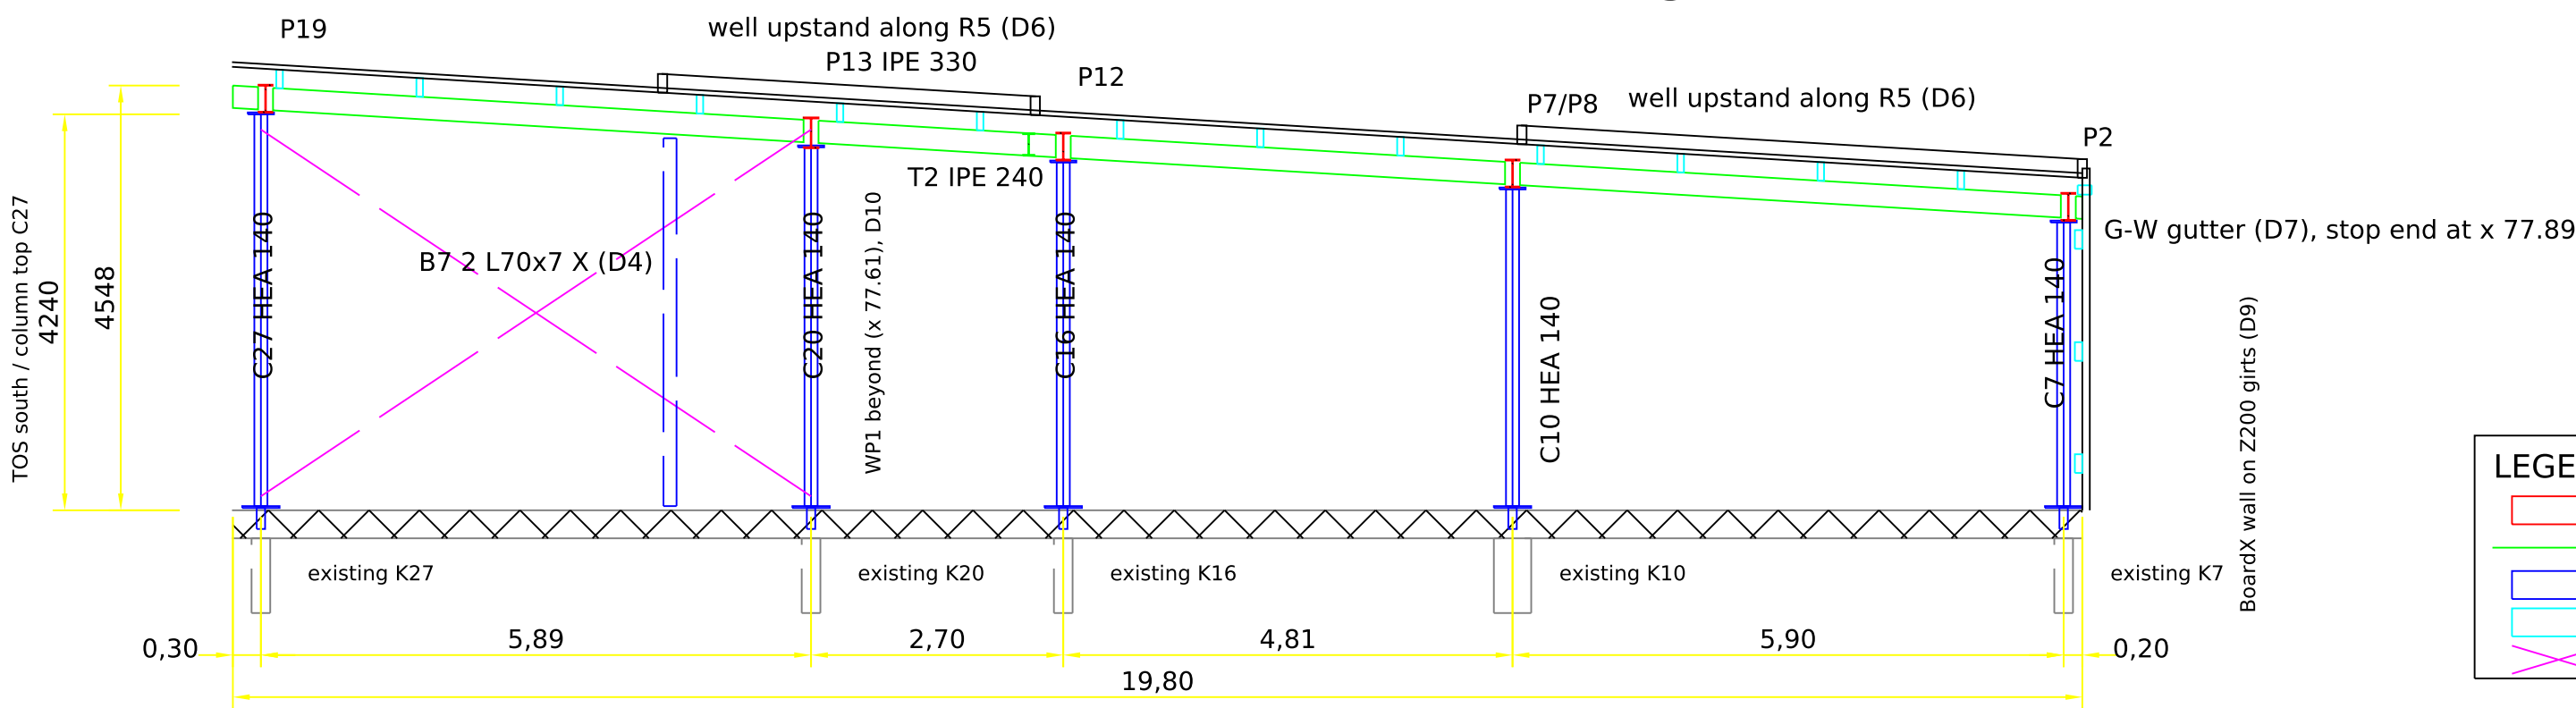

- LEGEND
- Primaries IPE 300 (P13 IPE 330)
 - Rafters IPE 240, T2
 - Columns HEA 140
 - Purlins Z200 + panel 50
 - Bracing B7

PROJECT
Steel roof - Administration Building, Regatta Tourist Village, Tripoli

ALTERNATIVE C - POST-AND-BEAM BRACED STEEL ROOF, SANDWICH PANELS
Client: Regatta Tourist Village, Tripoli Issued by: Eng. MALEK ABOZRAIG (malek.abozraig@gmail.com) Units: m

SHEET TITLE
TYPICAL SECTIONS A-A, B-B, C-C

Sections 1:1 in model space (m); levels in mm; print 1:100 on A1
Status: ISSUED FOR CONSTRUCTION subject to the site verification of S00 section 9

REVISIONS			
3	2026-09-29	Rev 6a (IPE 300/240, HEA 140), bases Rev 8, bracing Rev 5a	
2	2026-09-28	Design Rev 3 / bases Rev 4b (critique C1-C15)	
1	2026-09-27	First issue: design Rev 2, bases Rev 3	

CURRENT REVISION
Rev 6a superstructure
Rev 8 bases / bracing Rev 5a
DATE 2026-09-29
Drawn: Designed:
Checked: Approved:

DRAWING No.
RTV-ST-S03

S03